

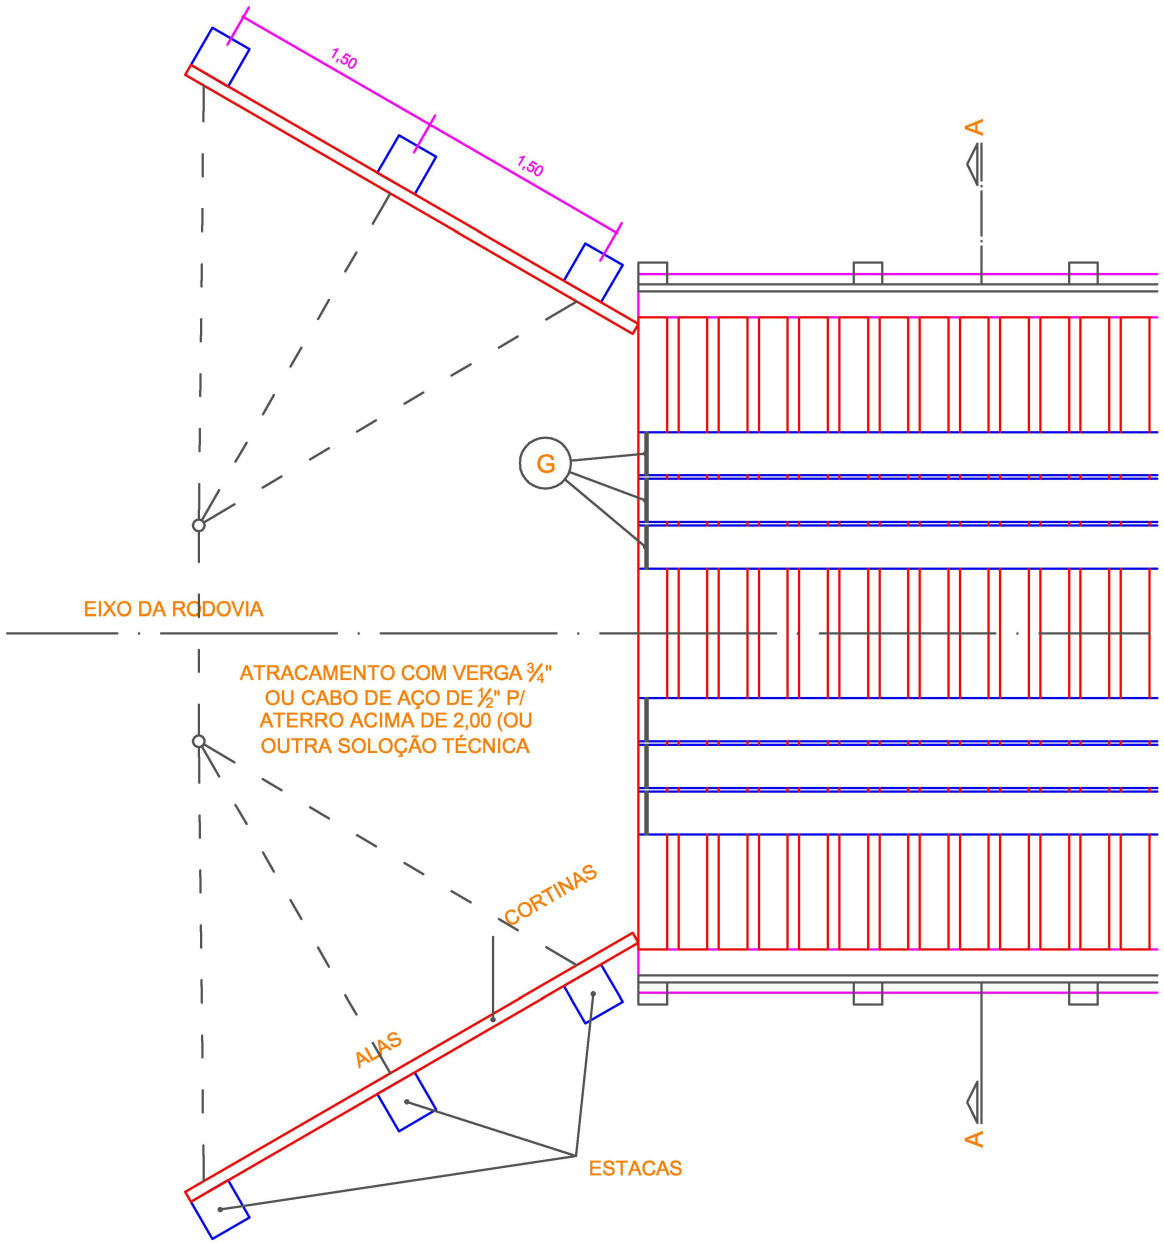


PEÇA	SEÇÃO
Estaca	(030 x 0,30) m
Transversina	(0,30 x 0,30) m
Linha D'água	(0,20 x 0,20) m
Balancins	(0,30 x 0,30) m
Contraventamento	(0,20 x 0,08) m
Mão Francesa	(0,20 x 0,20) m
Longarinas	(0,30 x 0,30) m
Pranchetas	(0,20 x 0,08) m
Guarda Rodas	(0,30 x 0,30) m
Deslizantes	(0,30 x 0,08) m
Guarda Corpo	((Corrimão (0,15 x 0,05) + (Balaústre 0,20 x 0,08)) m


PROJETO DE PONTE DE MADEIRA - VÃO 6m PLANTA	FL: 1/5
DNIT - DEPARTAMENTO NACIONAL DE INFRAESTRUTURA DE TRANSPORTES COORDENAÇÃO DE ENGENHARIA/SRDNIT/AM ENG. CIVIL EDSON MOREIRA CAVALCANTE	ESCALA: 1:50 DATA: JAN/18

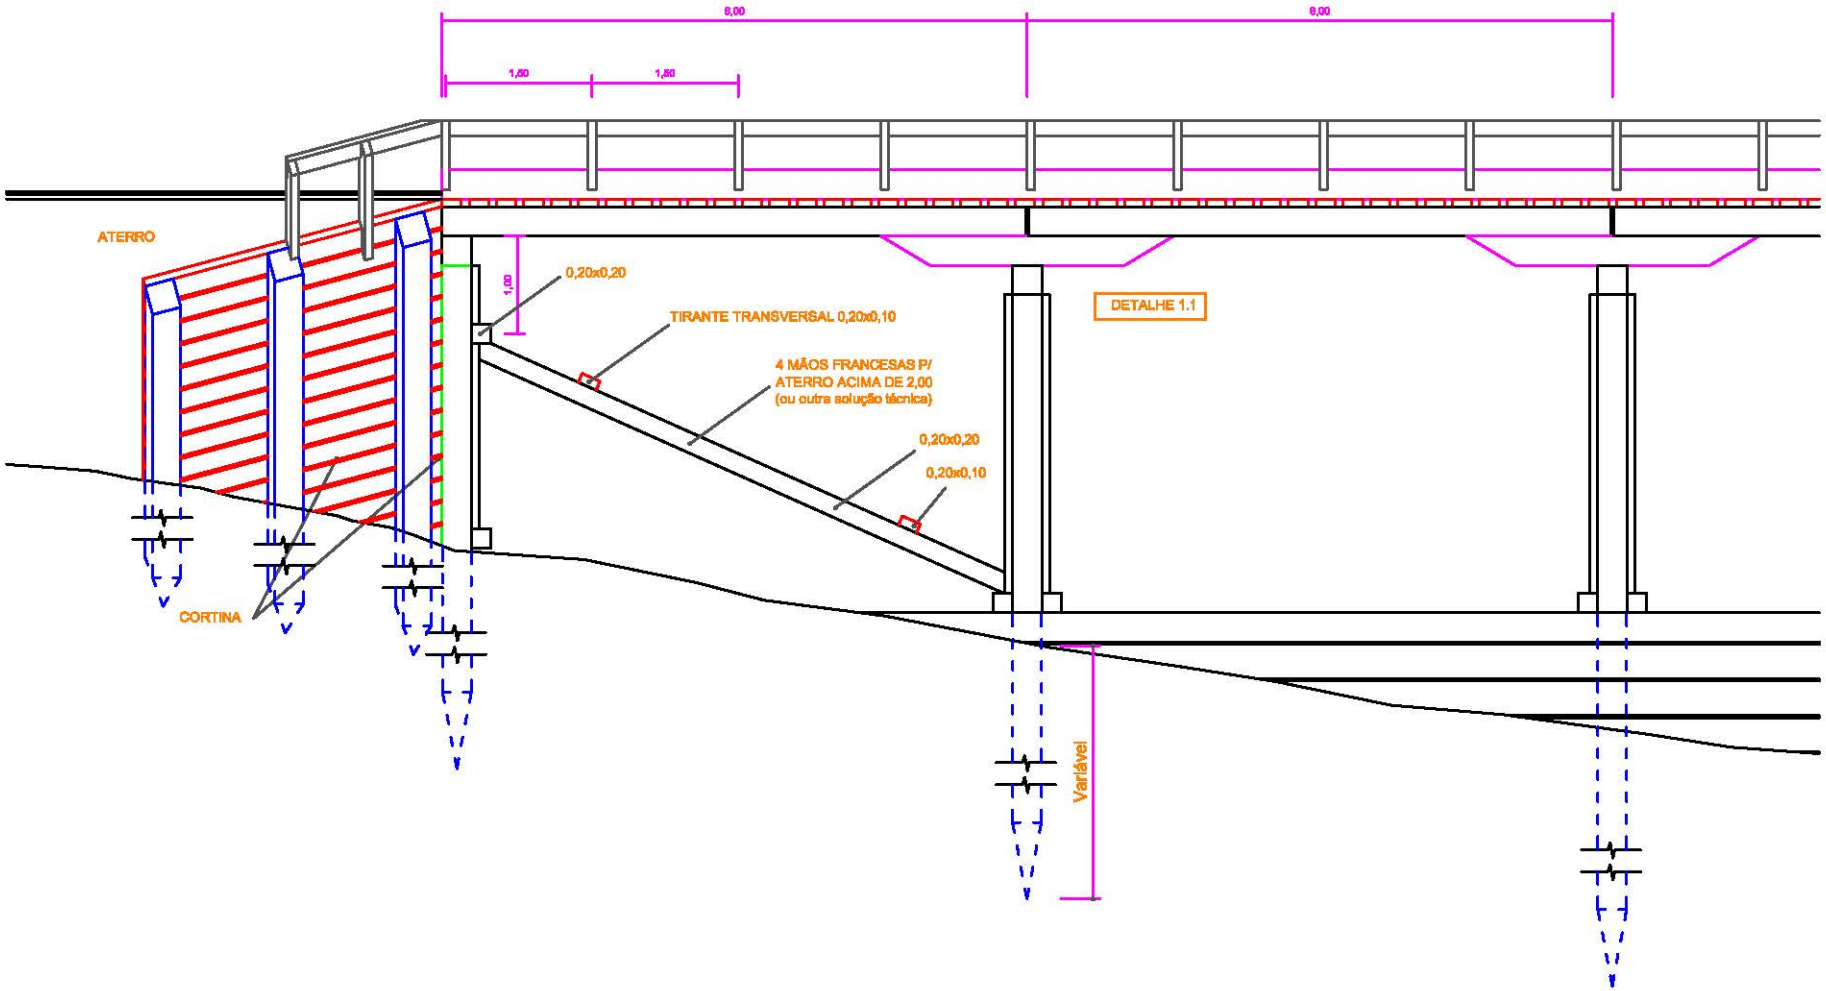

PROJETO DE PONTE DE MADEIRA - VÃO 6m VISTA LATERAL	FL: 2/5
DNIT - DEPARTAMENTO NACIONAL DE INFRAESTRUTURA DE TRANSPORTES COORDENAÇÃO DE ENGENHARIA/SRDNIT/AM ENG. CIVIL EDSON MOREIRA CAVALCANTE	ESCALA: 1:75 DATA: JAN/18

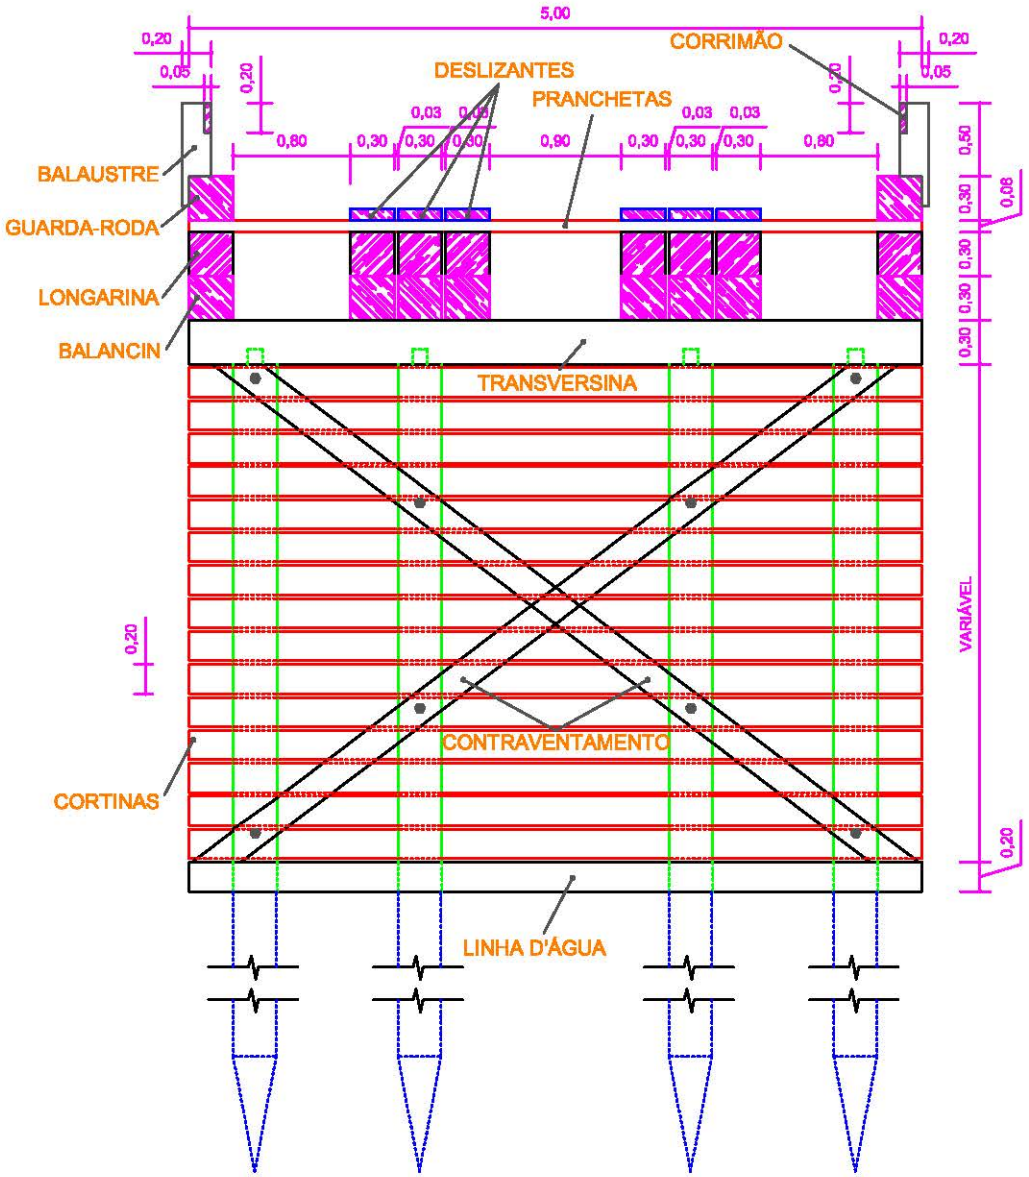

PROJETO DE PONTE DE MADEIRA - VÃO 6m CORTE A-A	FL: 3/5
DNIT - DEPARTAMENTO NACIONAL DE INFRAESTRUTURA DE TRANSPORTES COORDENAÇÃO DE ENGENHARIA/SRDNIT/AM ENG. CIVIL EDSON MOREIRA CAVALCANTE	ESCALA: 1:50 DATA: JAN/18

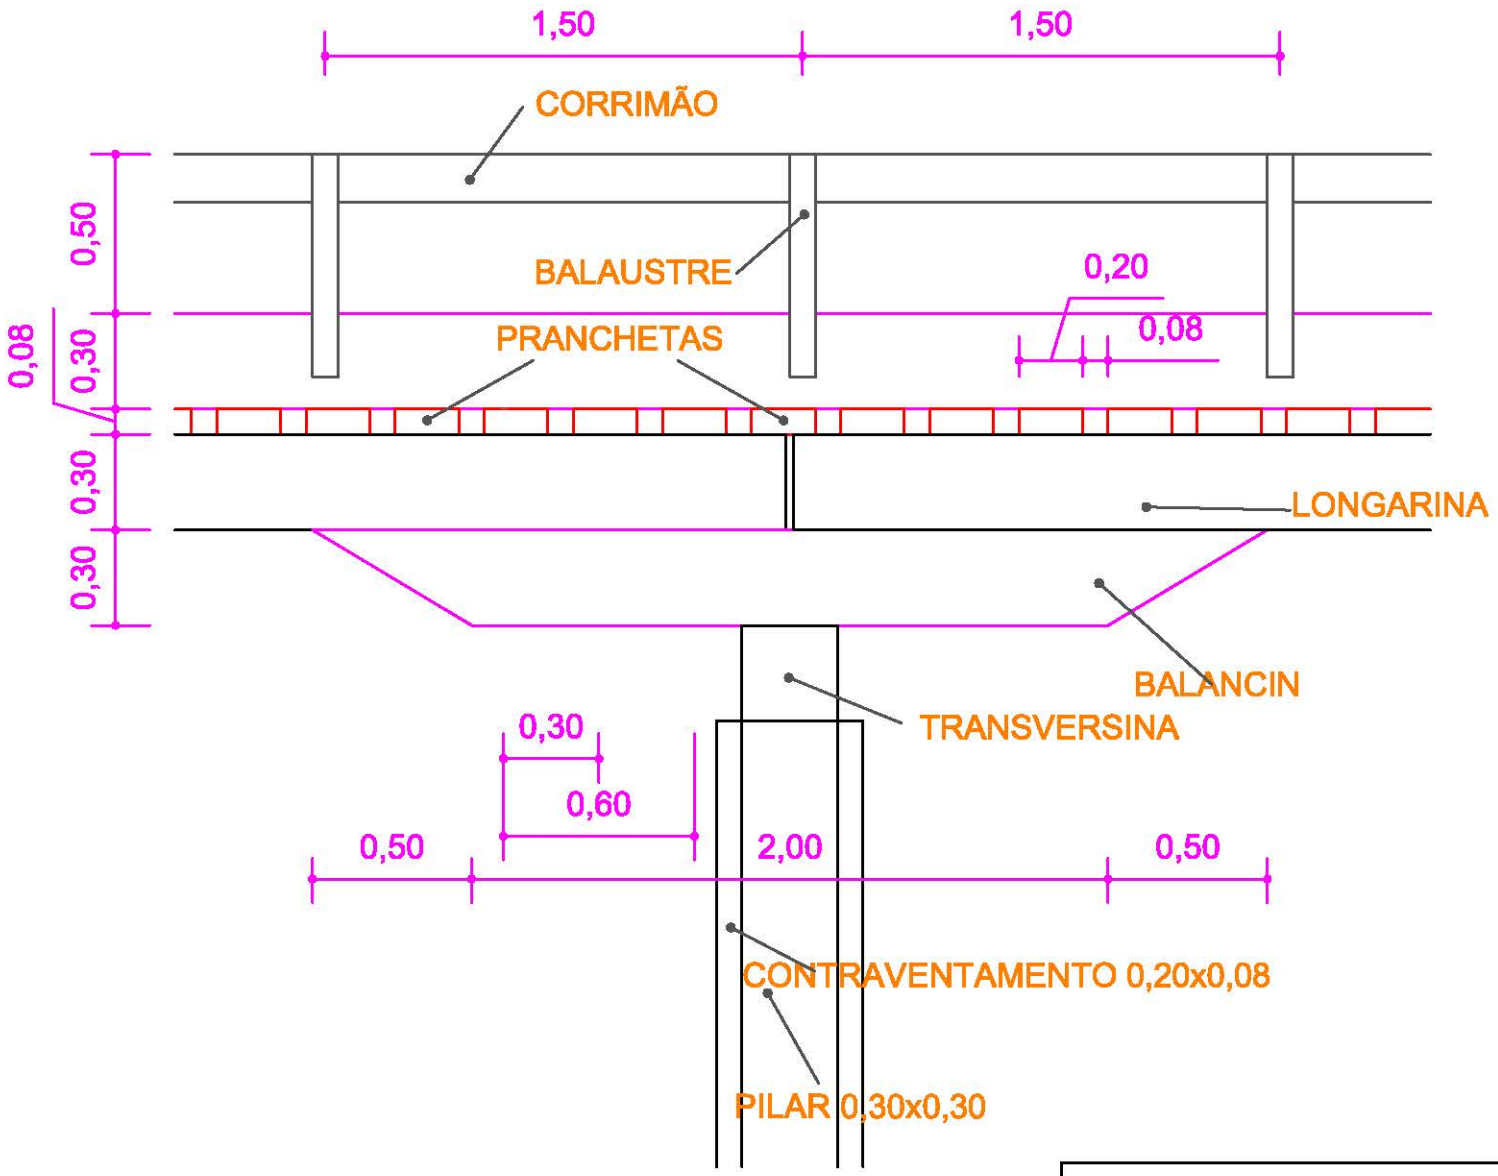

PROJETO DE PONTE DE MADEIRA - VÃO 6m DETALHE 1-1	FL: 4/5
DNIT - DEPARTAMENTO NACIONAL DE INFRAESTRUTURA DE TRANSPORTES COORDENAÇÃO DE ENGENHARIA/SRDNIT/AM ENG. CIVIL EDSON MOREIRA CAVALCANTE	ESCALA: 1:20 DATA: JAN/18

MEMORIA DE CALCULO - FERRAGENS PARA PONTE DE MADEIRA

FERRAGENS PARA PONTE DE MADEIRA (VÃO DE 6,00 m)

PERNETES AÇO CA-50

PEÇA DE MADEIRA	UND	Comprimento da peça	Quantidades de pernetes	Comprimento do pernete	Diametro	Comp. Total de pernete	Comp. Total de pernete por peça	Fator	Peso
			und	(m)	ø	(m)	(m)	(kg/m)	(kg)
Transversinas (seção)	m	5,00	4,00	0,60	5/8"	2,400	0,480	1,548	0,7430
Balancins (seção)	m	2,50	8,00	0,60	5/8"	4,800	1,920	1,548	2,9722
Longarinas (vão)	m	6,00	16,00	0,60	5/8"	9,600	1,600	1,548	2,4768
Guarda rodas (vão)	m	6,00	6,00	0,50	5/8"	3,000	0,500	1,548	0,7740
Deslizantes (vão)	m	6,00	36,00	0,40	5/16"	14,400	2,400	0,383	0,9192
Contraventamento (seção)	m	7,50	8,00	0,50	5/8"	4,000	0,533	1,548	0,8256
Linha d´água (seção)	m	5,00	8,00	0,50	5/8"	4,000	0,800	1,548	1,2384
Mão francesa (seção)	m	8,00	2,00	0,30	5/8"	0,600	0,075	1,548	0,1161
Guarda corpo - Alas (balaústre)	m	6,00	24,00	0,20	5/16"	4,800	0,800	0,383	0,3064
Guarda corpo (vão) (balaústre)	m	6,00	32,00	0,15	5/16"	4,800	0,800	0,383	0,3064
Alas	m²	11,00	12,00	0,50	5/8"	6,000	0,545	1,548	0,8444
								TOTAL	**11,52**

PREGOS

PEÇA DE MADEIRA	COMPRIMENTO	QUANTIDADE DE PREGO/M	PESO/UND	DIMENSÃO DO PREGO	PESO
	(m)	(m)	(m)	(mm)	(kg)
Deslizantes	1,00	2,000	0,0714	(25 x 72)	0,1429
Pranchetas	1,00	1,600	0,0400	(24 x 60)	0,0640
Guarda corpo (corrimão)	1,00	3,330	0,0082	(24 x 60)	0,0273
				TOTAL	**0,21**

PROJETO DE PONTE DE MADEIRA - VÃO 6m FERRAGENS	FL: 5/5
DNIT - DEPARTAMENTO NACIONAL DE INFRAESTRUTURA DE TRANSPORTES COORDENAÇÃO DE ENGENHARIA/SRDNIT/AM ENG. CIVIL EDSON MOREIRA CAVALCANTE	ESCALA: IND. DATA: JAN/18